


Neighborhood parks in Al Warqa and al Mizhar Area Group C - PJ 20178 - Dubai Municipality


LIGHTING DESIGN PROPOSAL

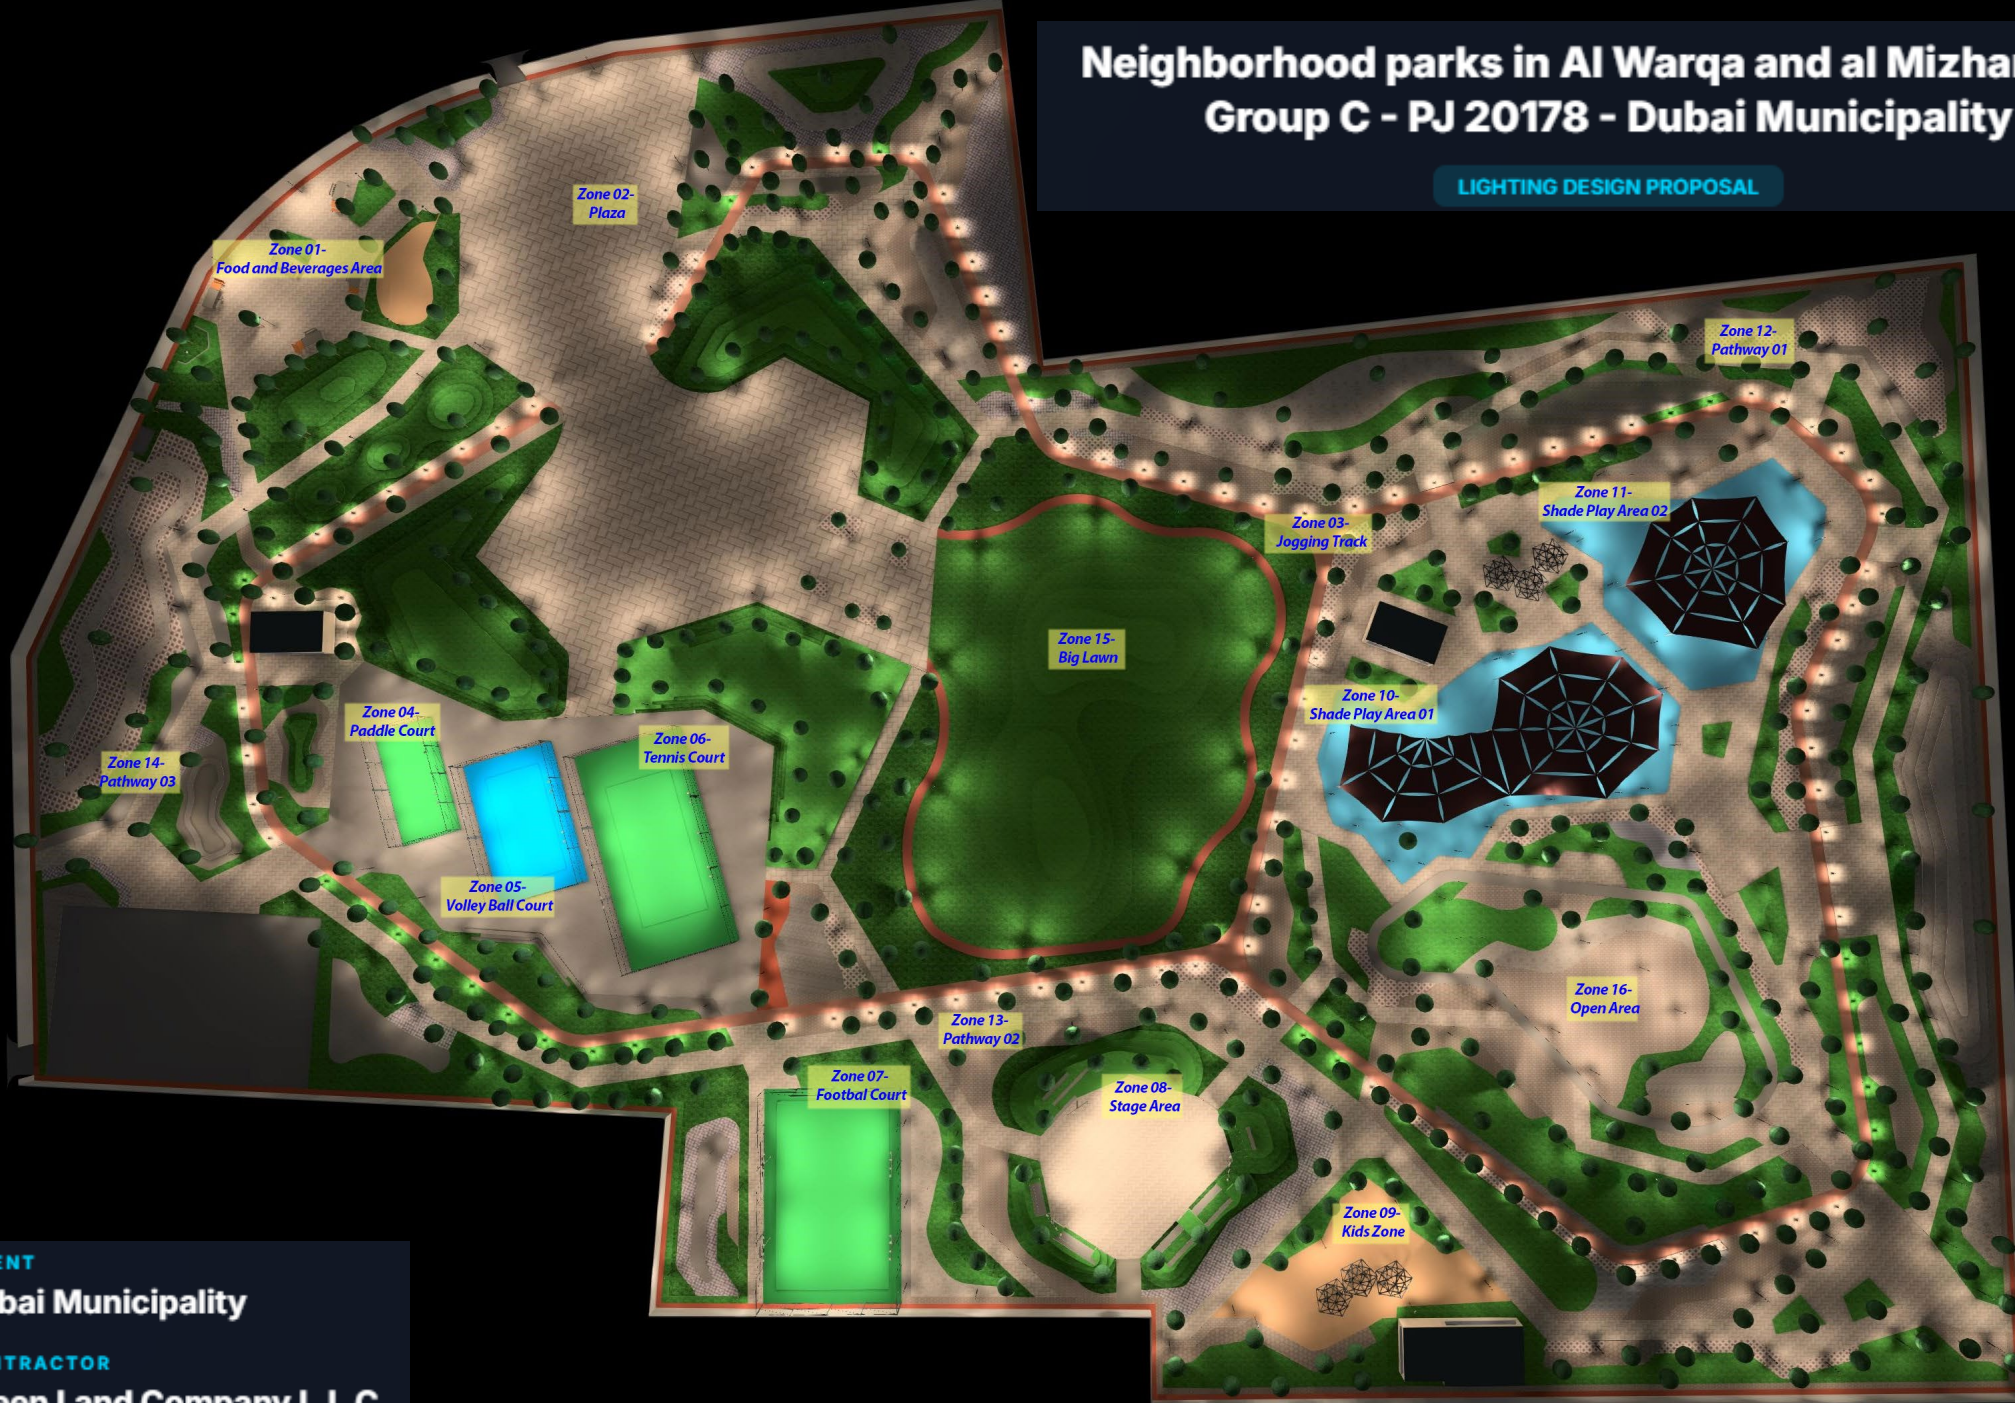

CLIENT
Dubai Municipality

CONTRACTOR
Green Land Company L.L.C

Zone 01- Food and Beverages Area

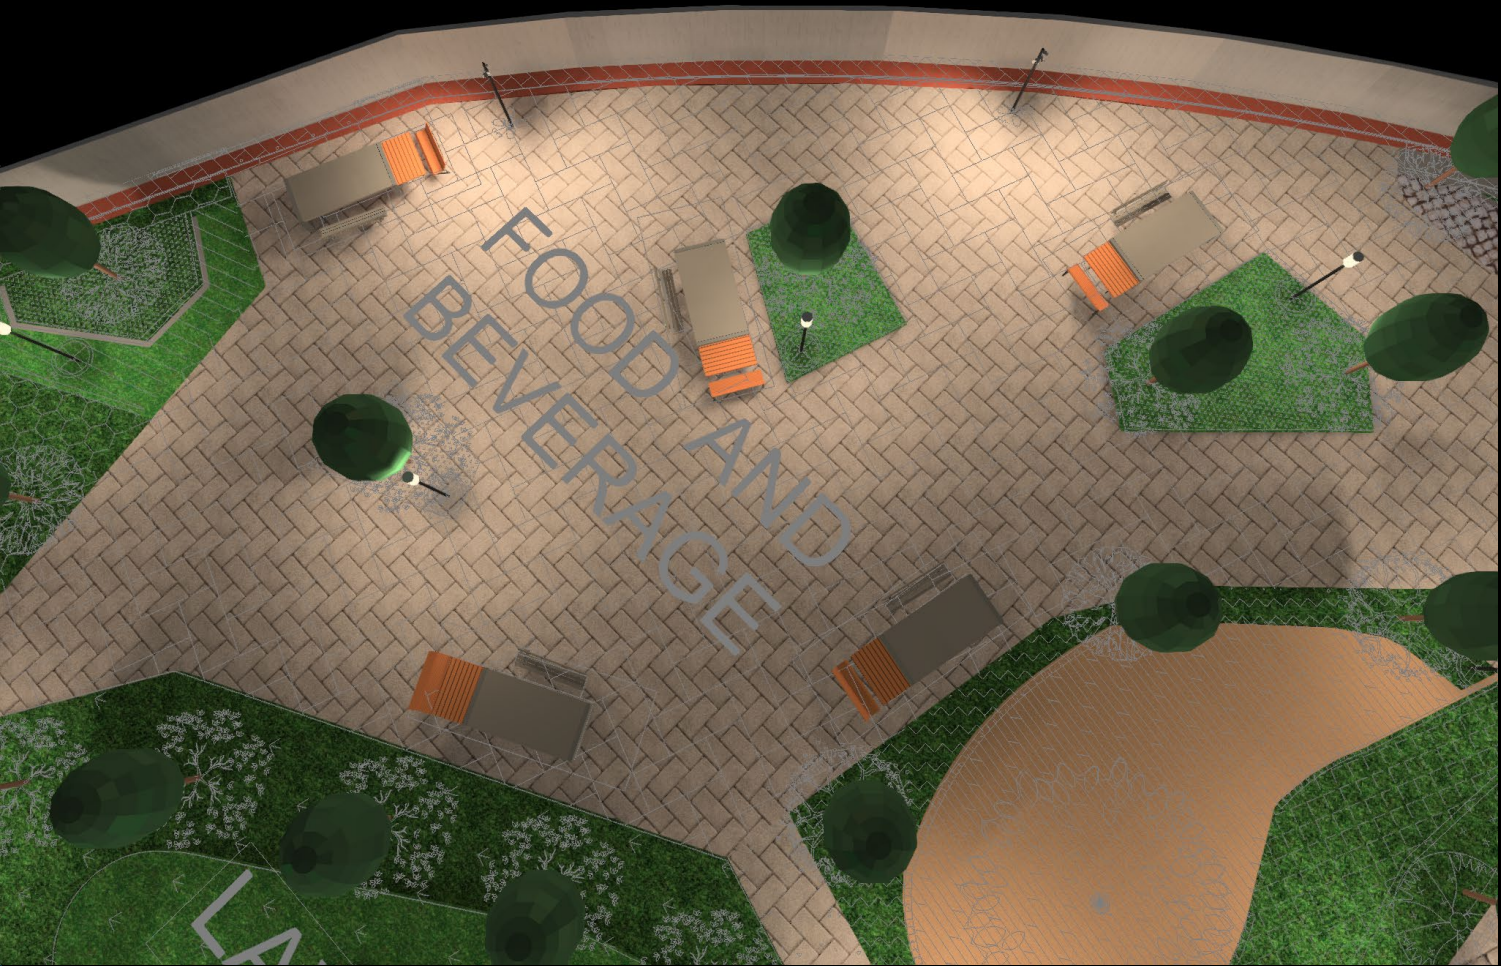

Properties

Ē

01- Food and Beverages Area
Perpendicular illuminance (adaptive)
Height: 0.100 m


17.8 lx

Type O-P2	Frater Spike Light SP02 25W 3000K 100Lm/W Black IP66 with on/off driver	8-10 weeks	SP02-025	
Type O-P1 & O-P2	Frater Post Top PT06 30W 3000K 120Lm/W IP65 Black with Dali Dimmable Driver	8-10 weeks	PT06-030	

Notes :

--

Zone 02- Plaza

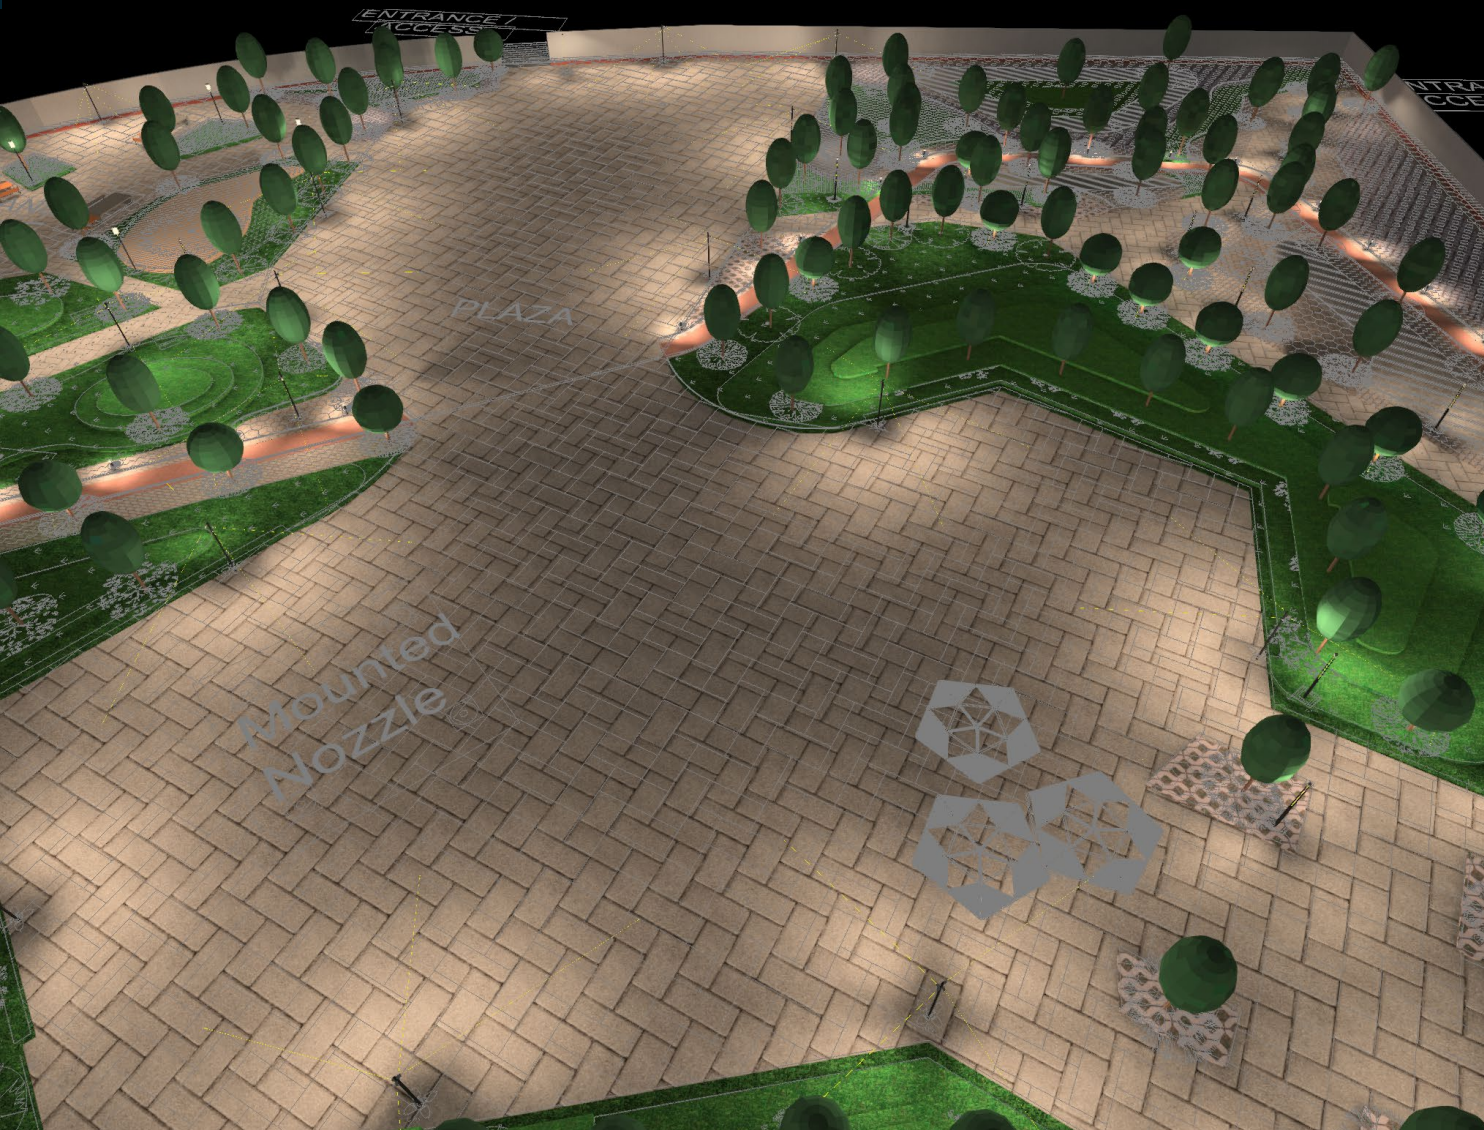

Properties


Ē

02- Plaza

12.8 lx

Perpendicular illuminance (adaptive)

Height: 0.100 m

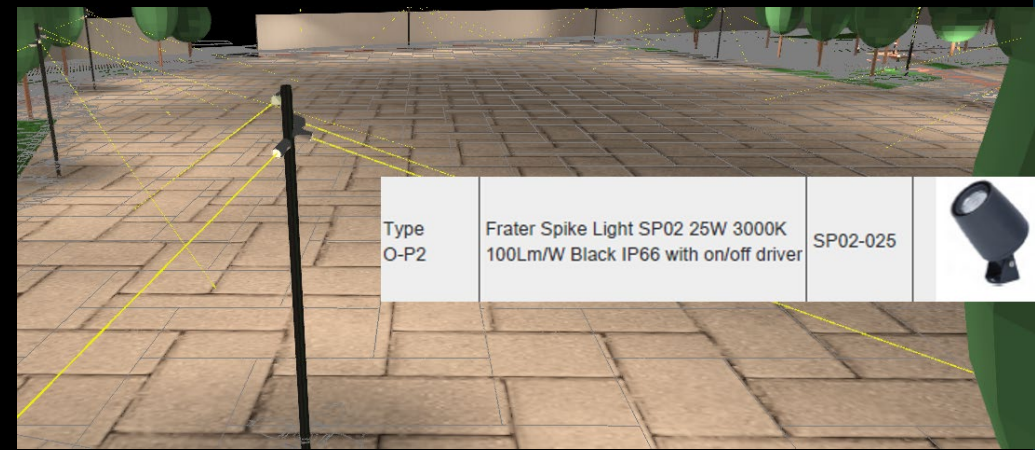

Type
O-P2

Frater Spike Light SP02 25W 3000K
100Lm/W Black IP66 with on/off driver

SP02-025



Notes :


CLIENT

Dubai Municipality

CONTRACTOR

Green Land Company L.L.C

Zone 03- Jogging Track

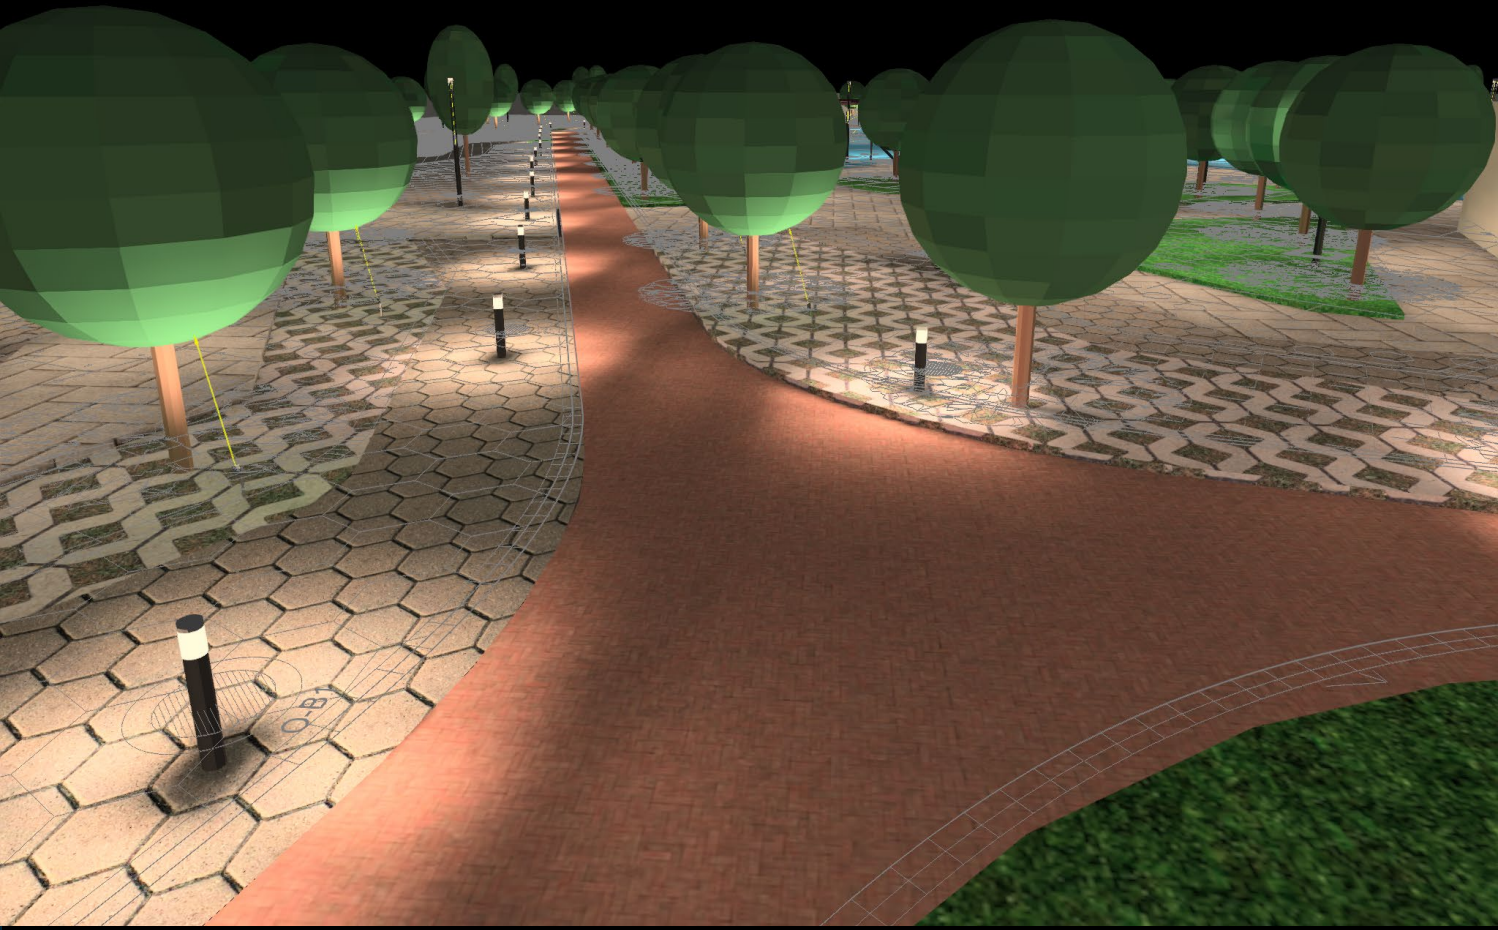


Properties

Ē

03- Jogging Track
Perpendicular illuminance (adaptive)
Height: 0.100 m


22.5 lx

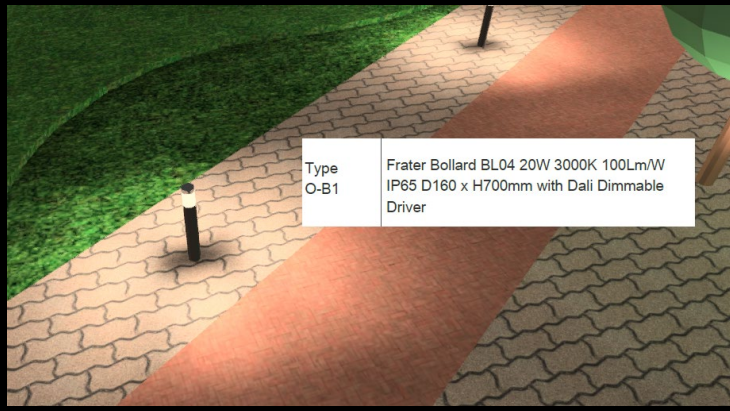

Type	Frater Bollard BL04 20W 3000K 100Lm/W
O-B1	IP65 D160 x H700mm with Dali Dimmable Driver

Notes :

Zone 04- Paddle Court

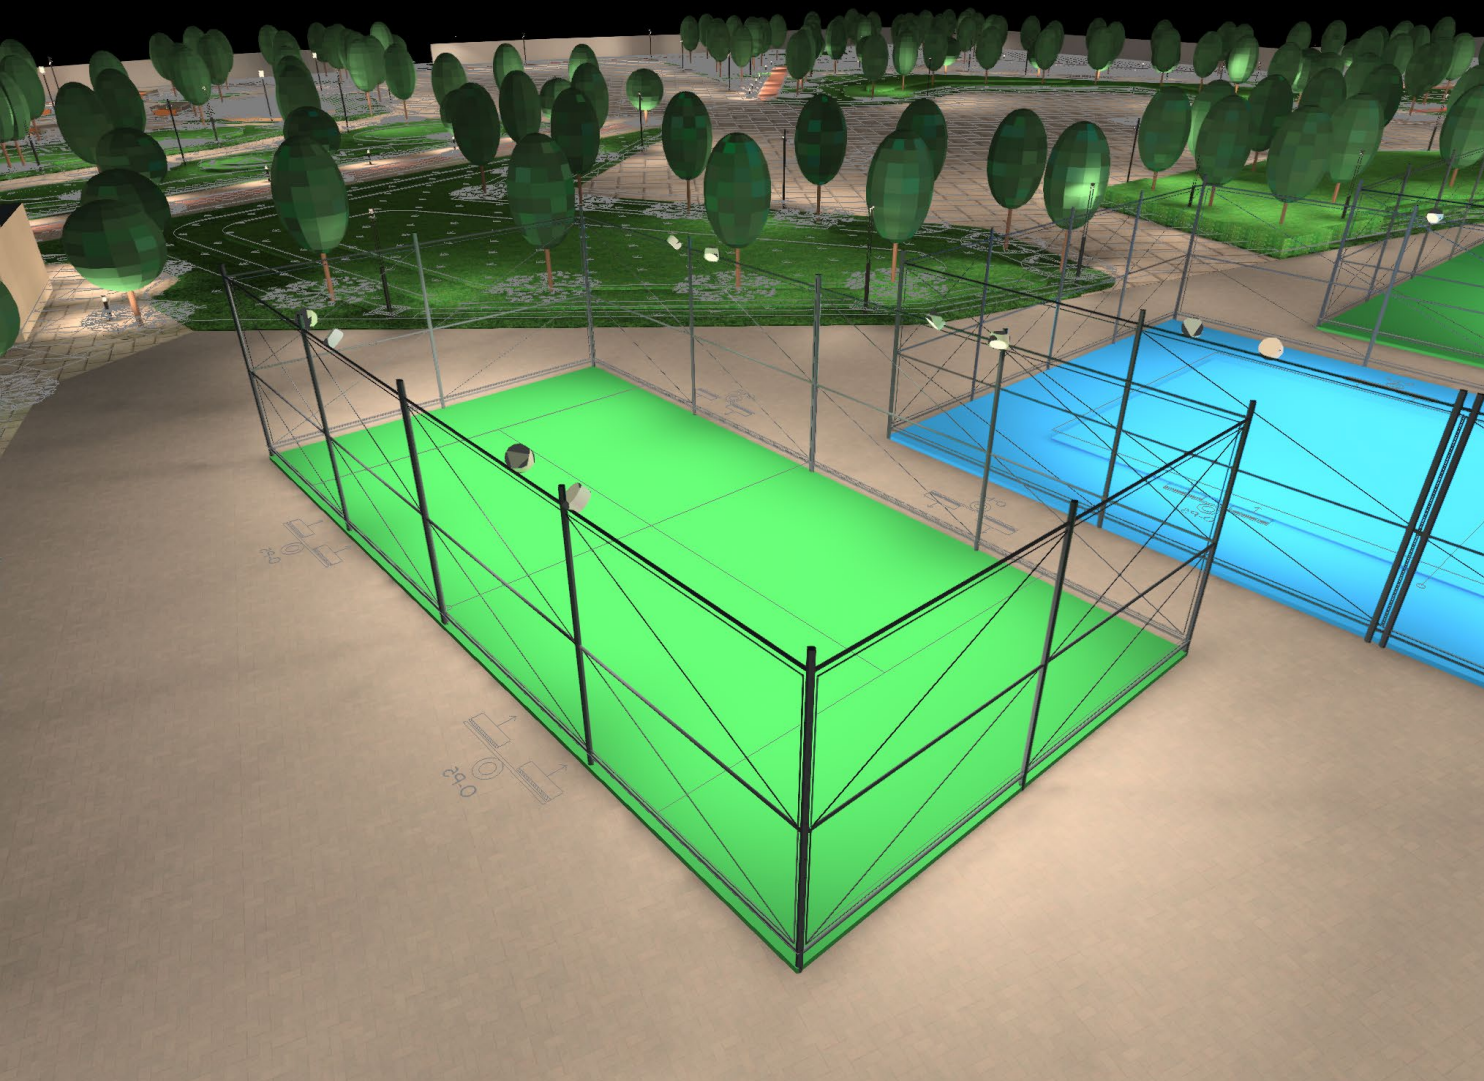


Properties

$\bar{E}$

04- Paddle Court
Perpendicular illuminance (adaptive)
Height: 0.200 m

325 lx

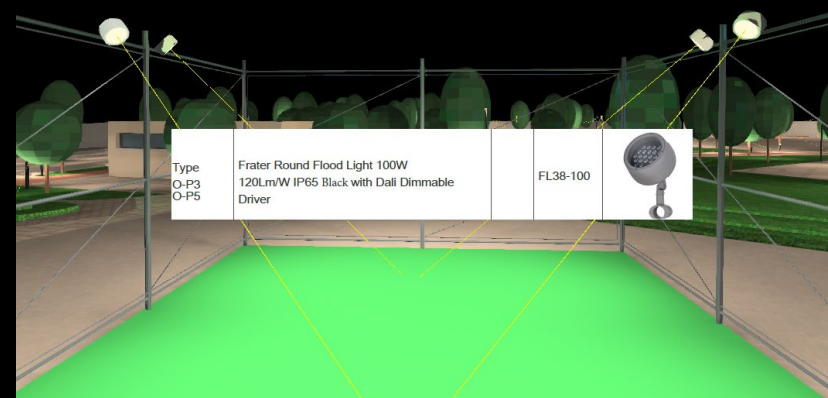

Type
O-P3
O-P5


Frater Round Flood Light 100W
120Lm/W IP65 Black with Dali Dimmable
Driver

FL38-100



Notes :

Zone 05- Volley Ball Court

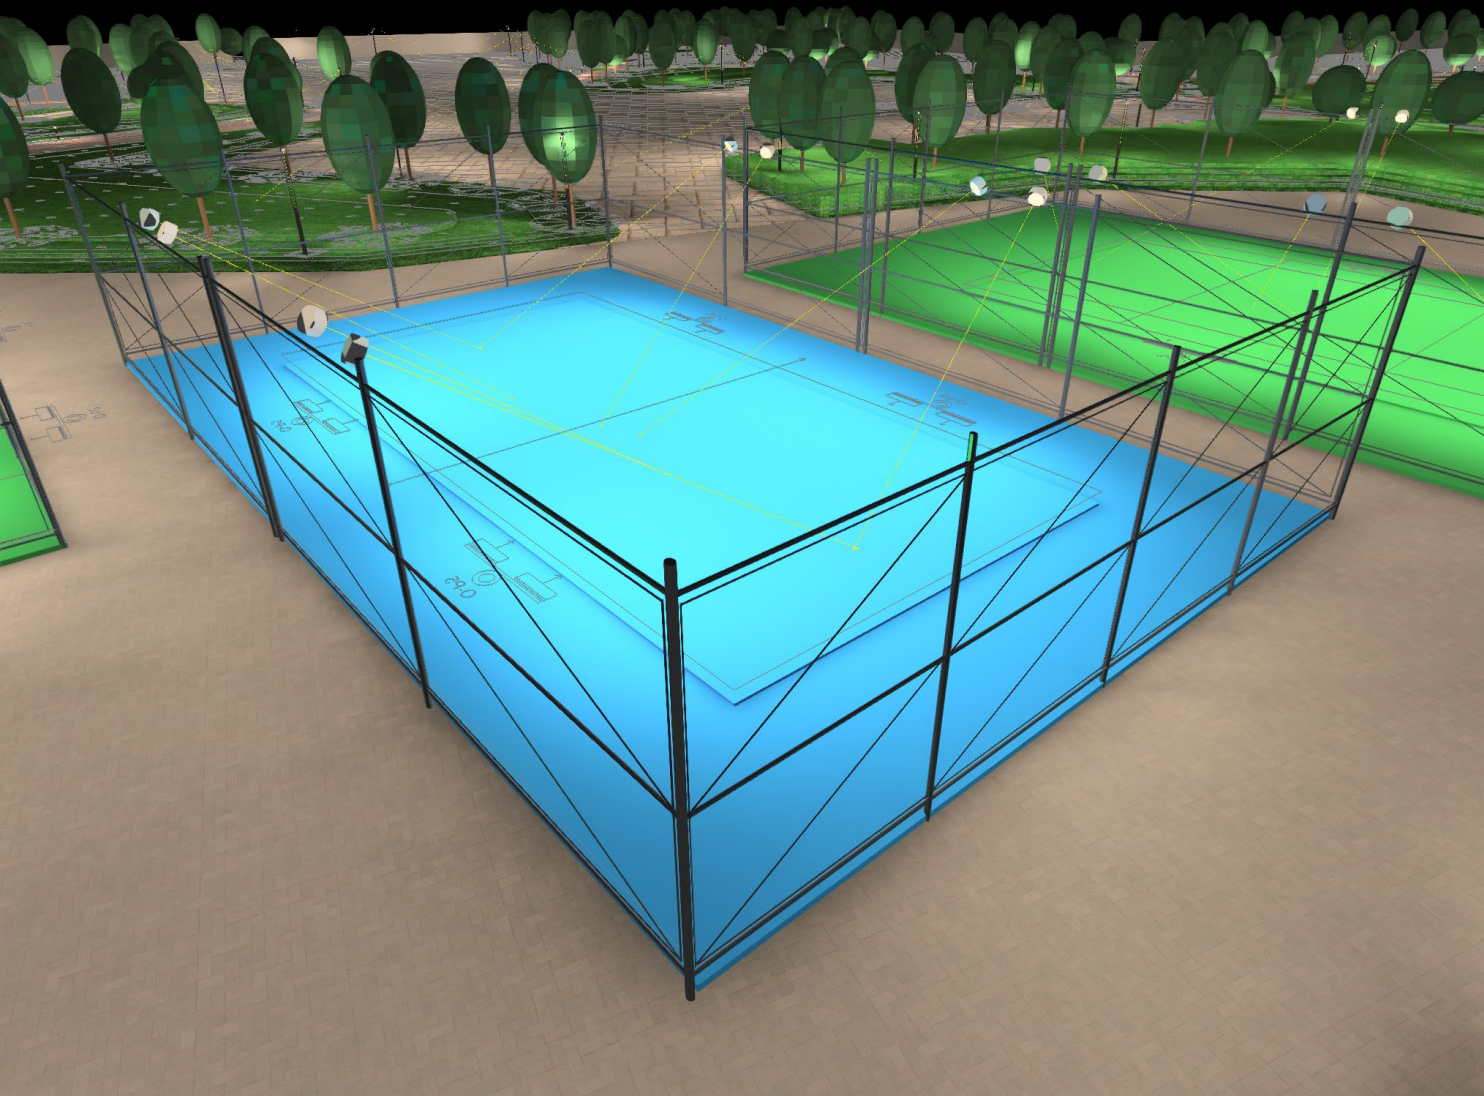


Properties

$\bar{E}$

05- Volley Ball Court
Perpendicular illuminance (adaptive)
Height: 0.250 m


272 lx

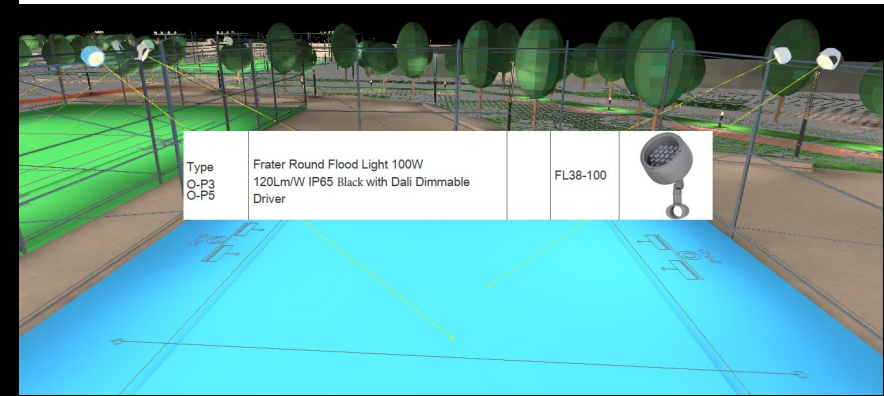

Type	Frater Round Flood Light 100W		
O-P3	120Lm/W IP65 Black with Dali Dimmable	FL38-100	
O-P5	Driver		

Notes :

Zone 06- Tennis Court

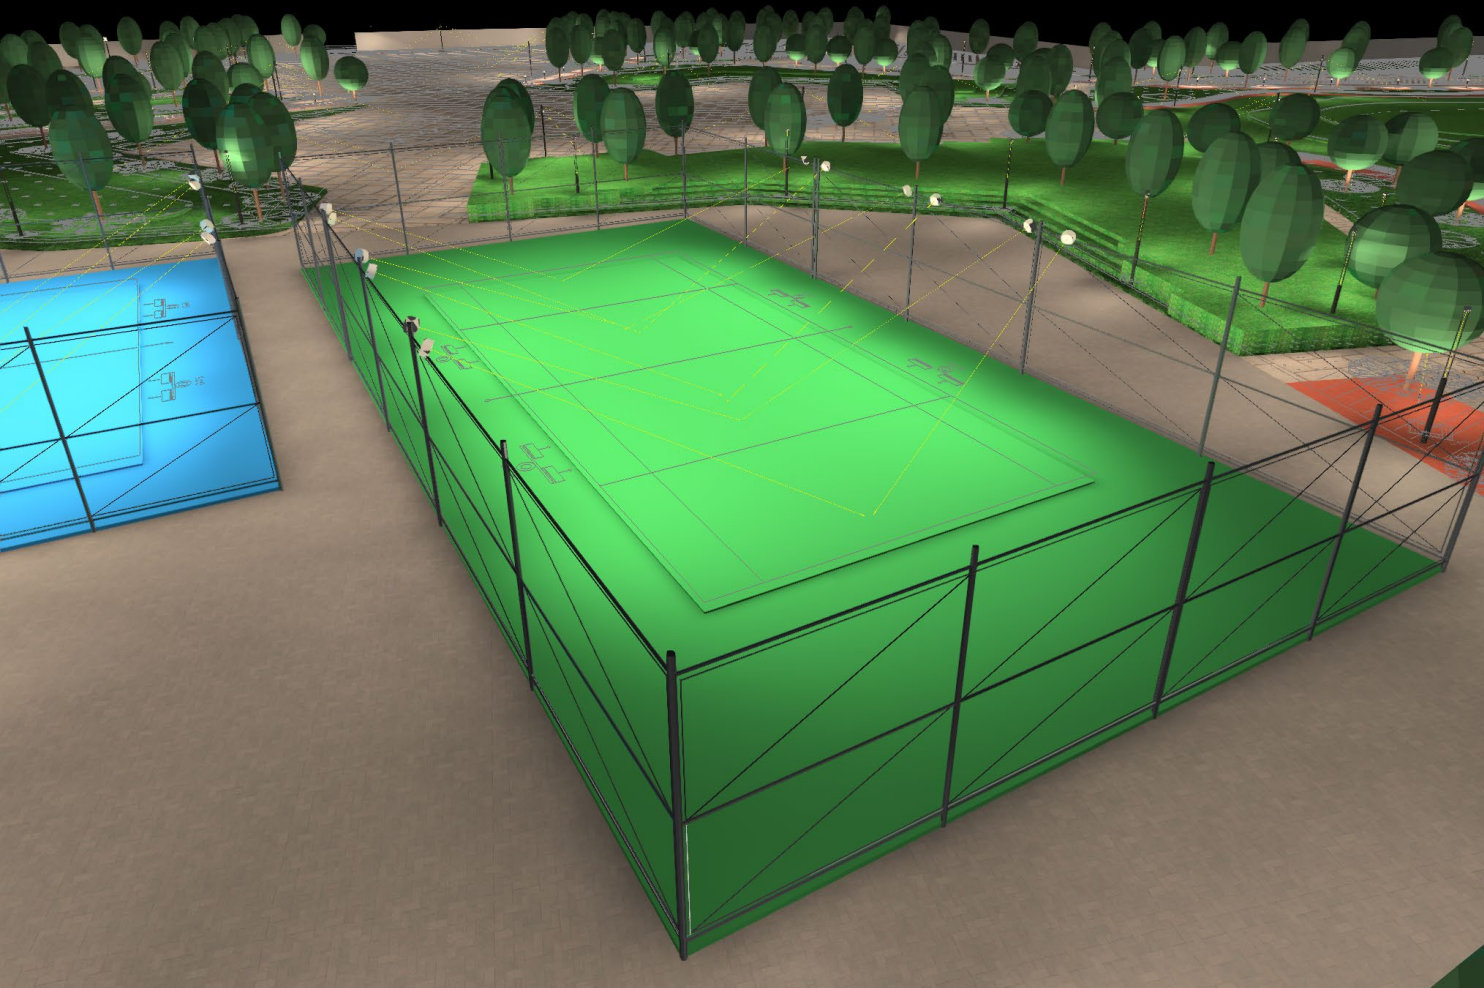


Properties

Ē


06- Tennis Court
Perpendicular illuminance (adaptive)
Height: 0.250 m

237 lx

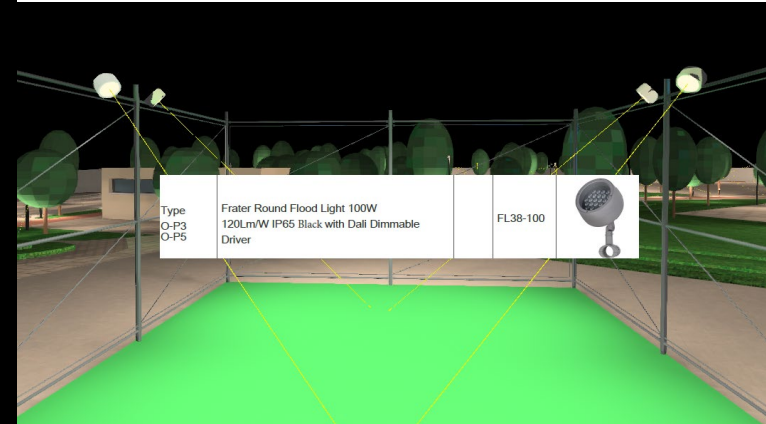

Notes :

Zone 07- Football Court

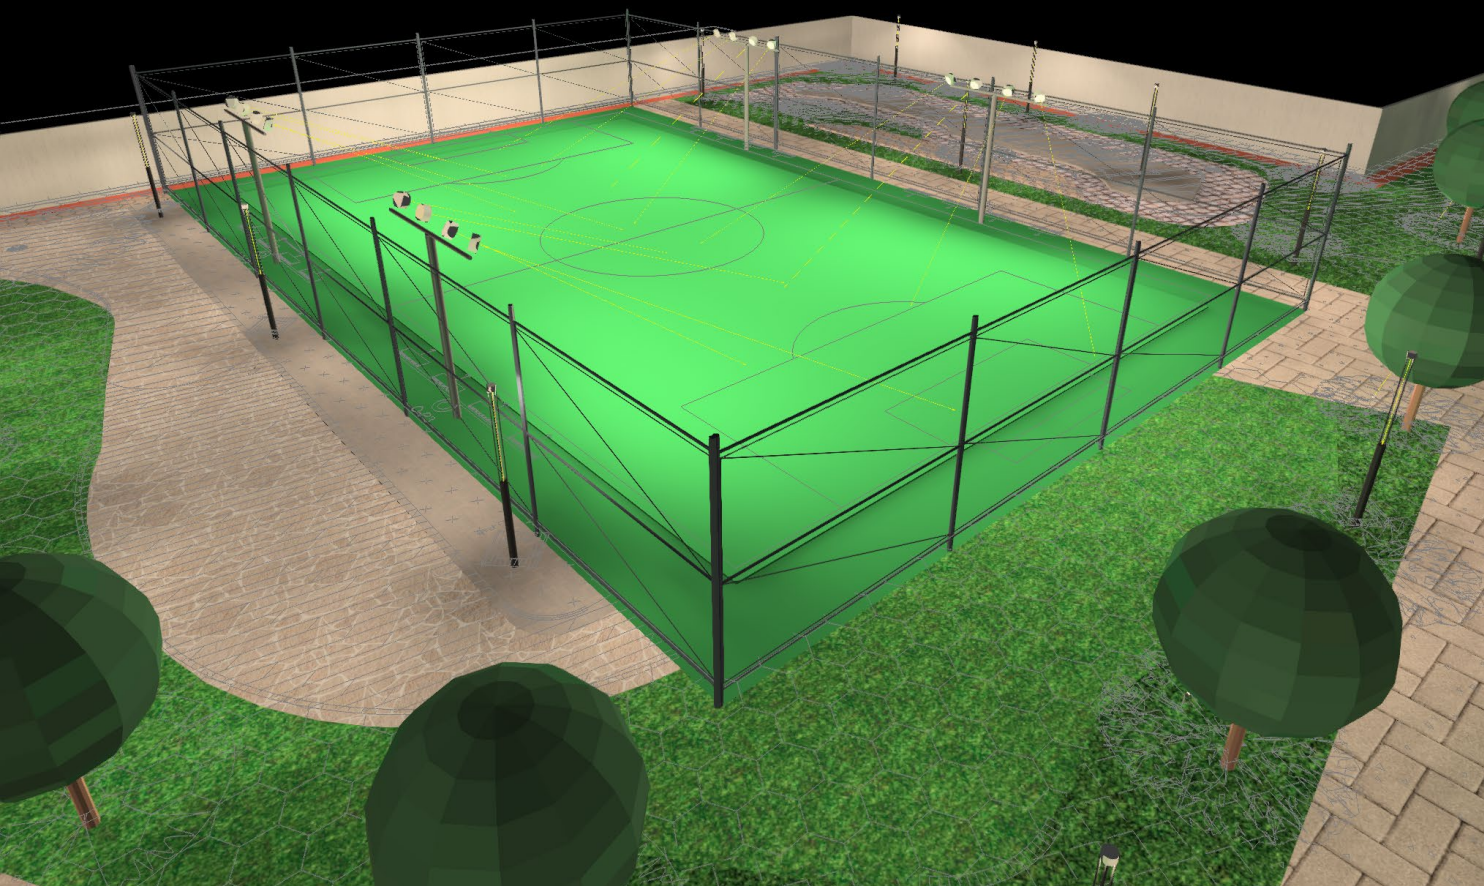


Properties

Ē

07- Football Court
Perpendicular illuminance (adaptive)
Height: 0.150 m

201 lx

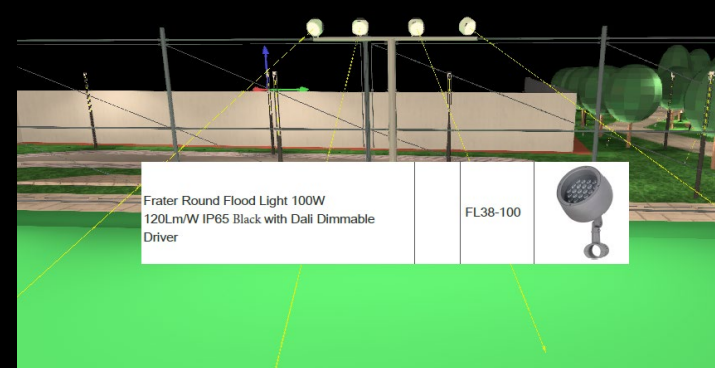


Frater Round Flood Light 100W
120Lm/W IP65 Black with Dali Dimmable
Driver

FL38-100



Notes :

Zone 08- Stage Area

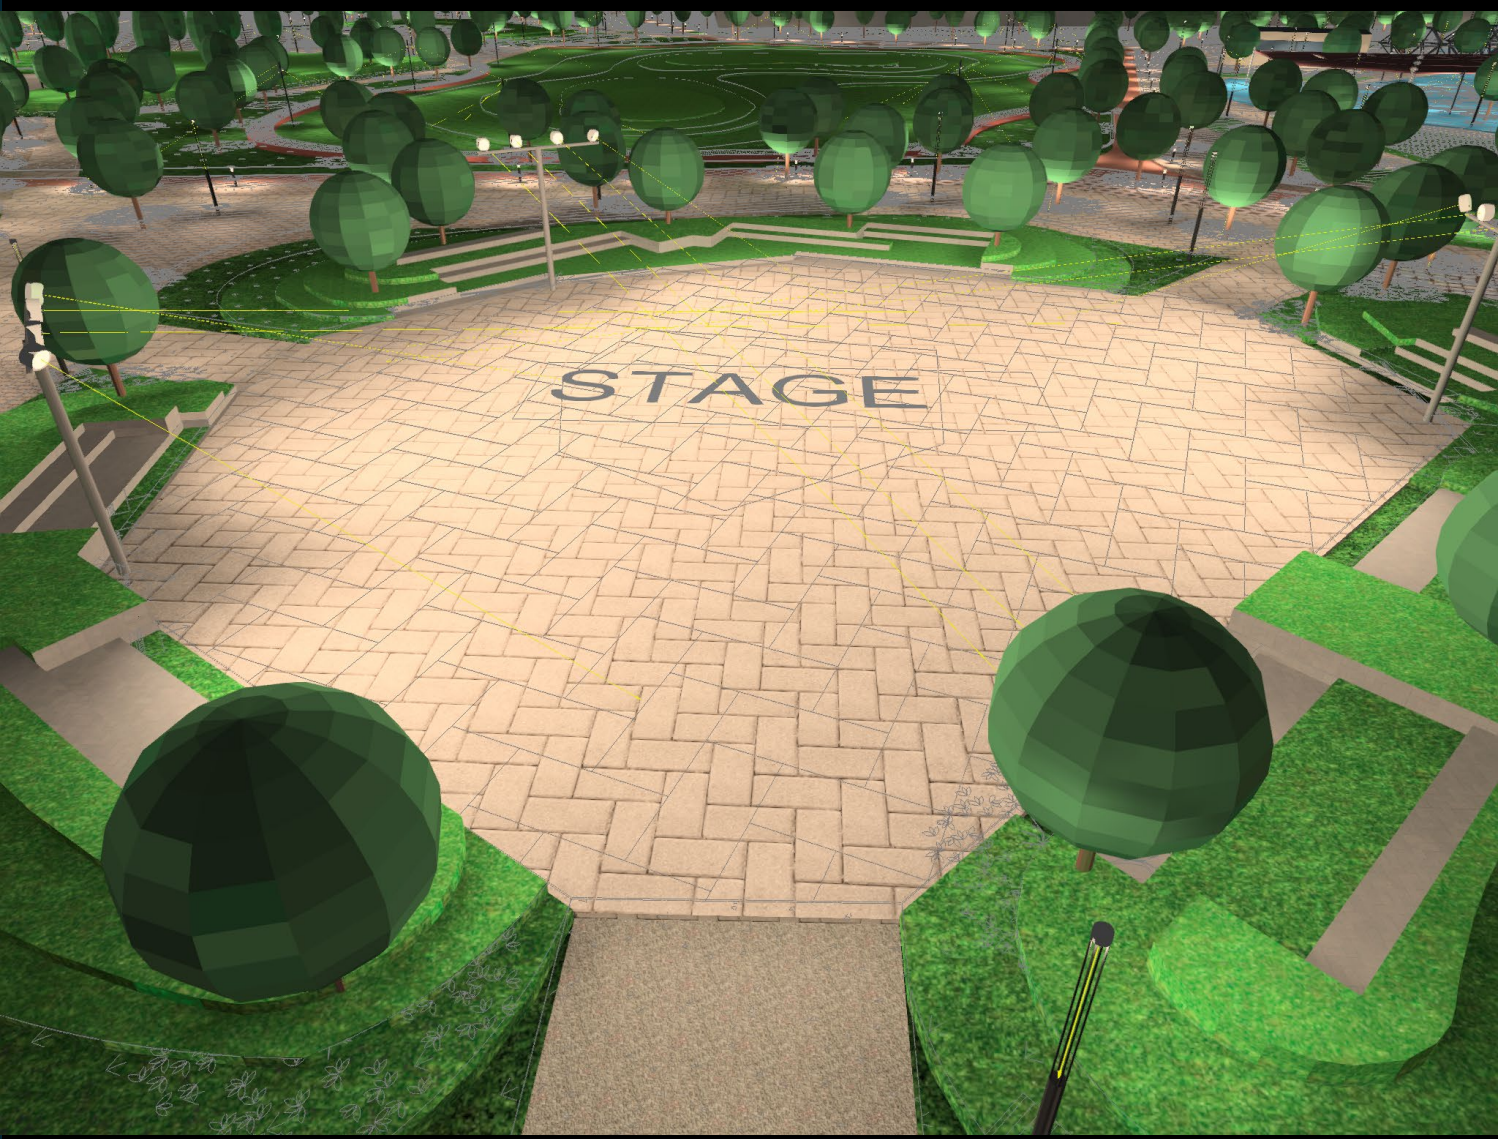

Properties

$\bar{E}$


08- Stage Area
Perpendicular illuminance (adaptive)
Height: 0.200 m

106 lx



Notes :

Zone 09- Kids Zone

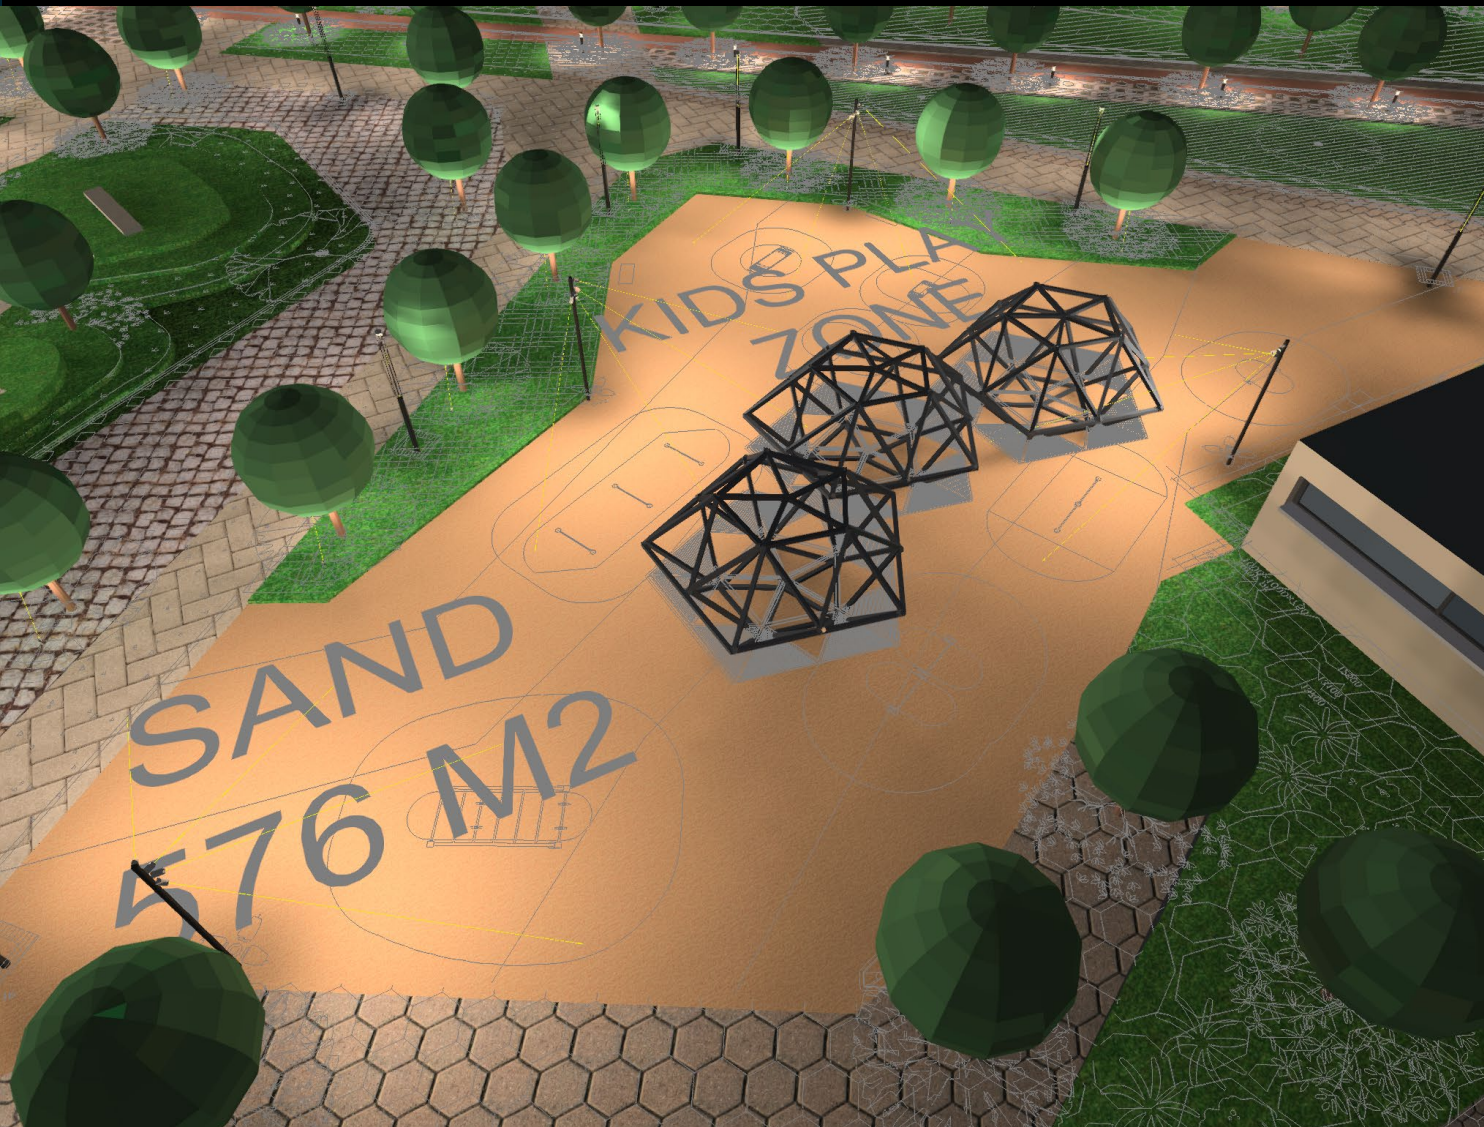

Properties

Ē

09- Kids Zone
Perpendicular illuminance (adaptive)
Height: 0.100 m


36.6 lx



Type O-P2	Frater Spike Light SP02 25W 3000K 100Lm/W Black IP66 with on/off driver	SP02-025	
--------------	--	----------	---

Notes :

Zone 10- Shade Play Area 01

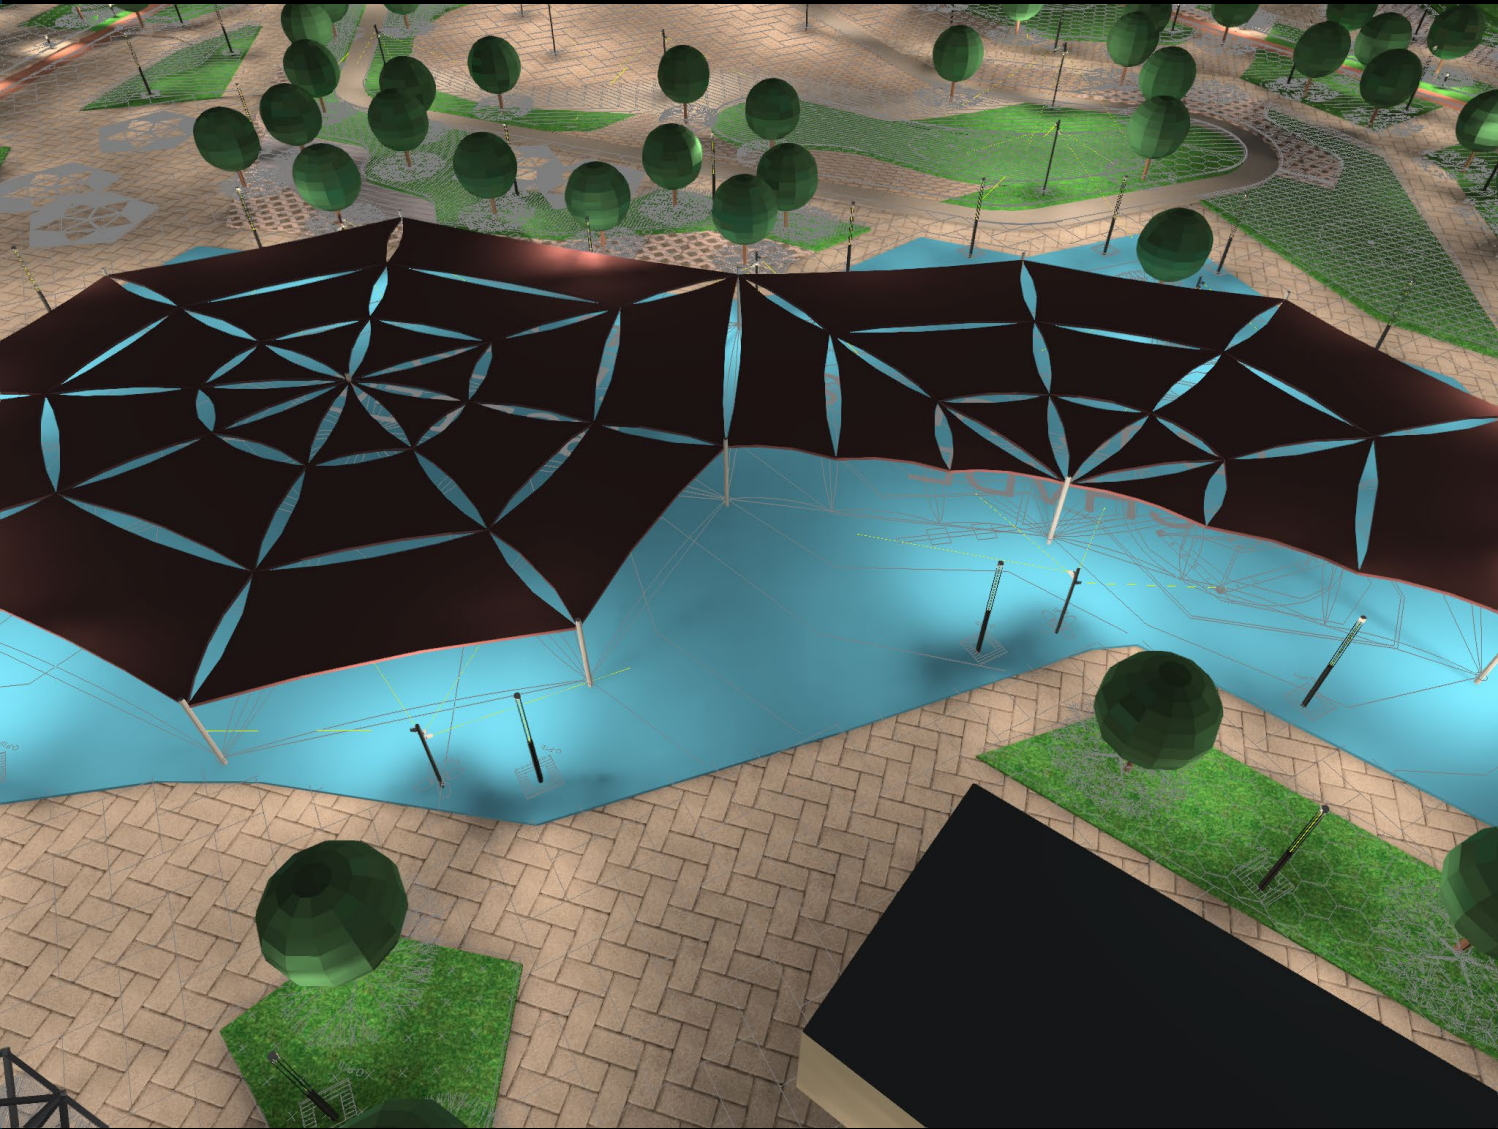


Properties

Ē

10- Shade Play Area 01
Perpendicular illuminance (adaptive)
Height: 0.200 m

37.2 lx

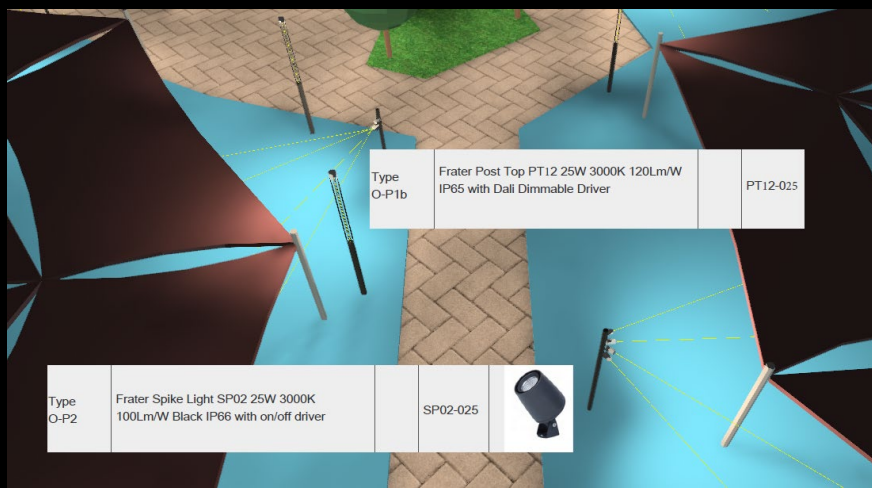


Type O-P1b	Frater Post Top PT12 25W 3000K 120Lm/W IP65 with Dali Dimmable Driver	PT12-025
---------------	--	----------

Type O-P2	Frater Spike Light SP02 25W 3000K 100Lm/W Black IP66 with on/off driver	SP02-025	
--------------	--	----------	---

Notes :

Zone 11- Shade Play Area 02

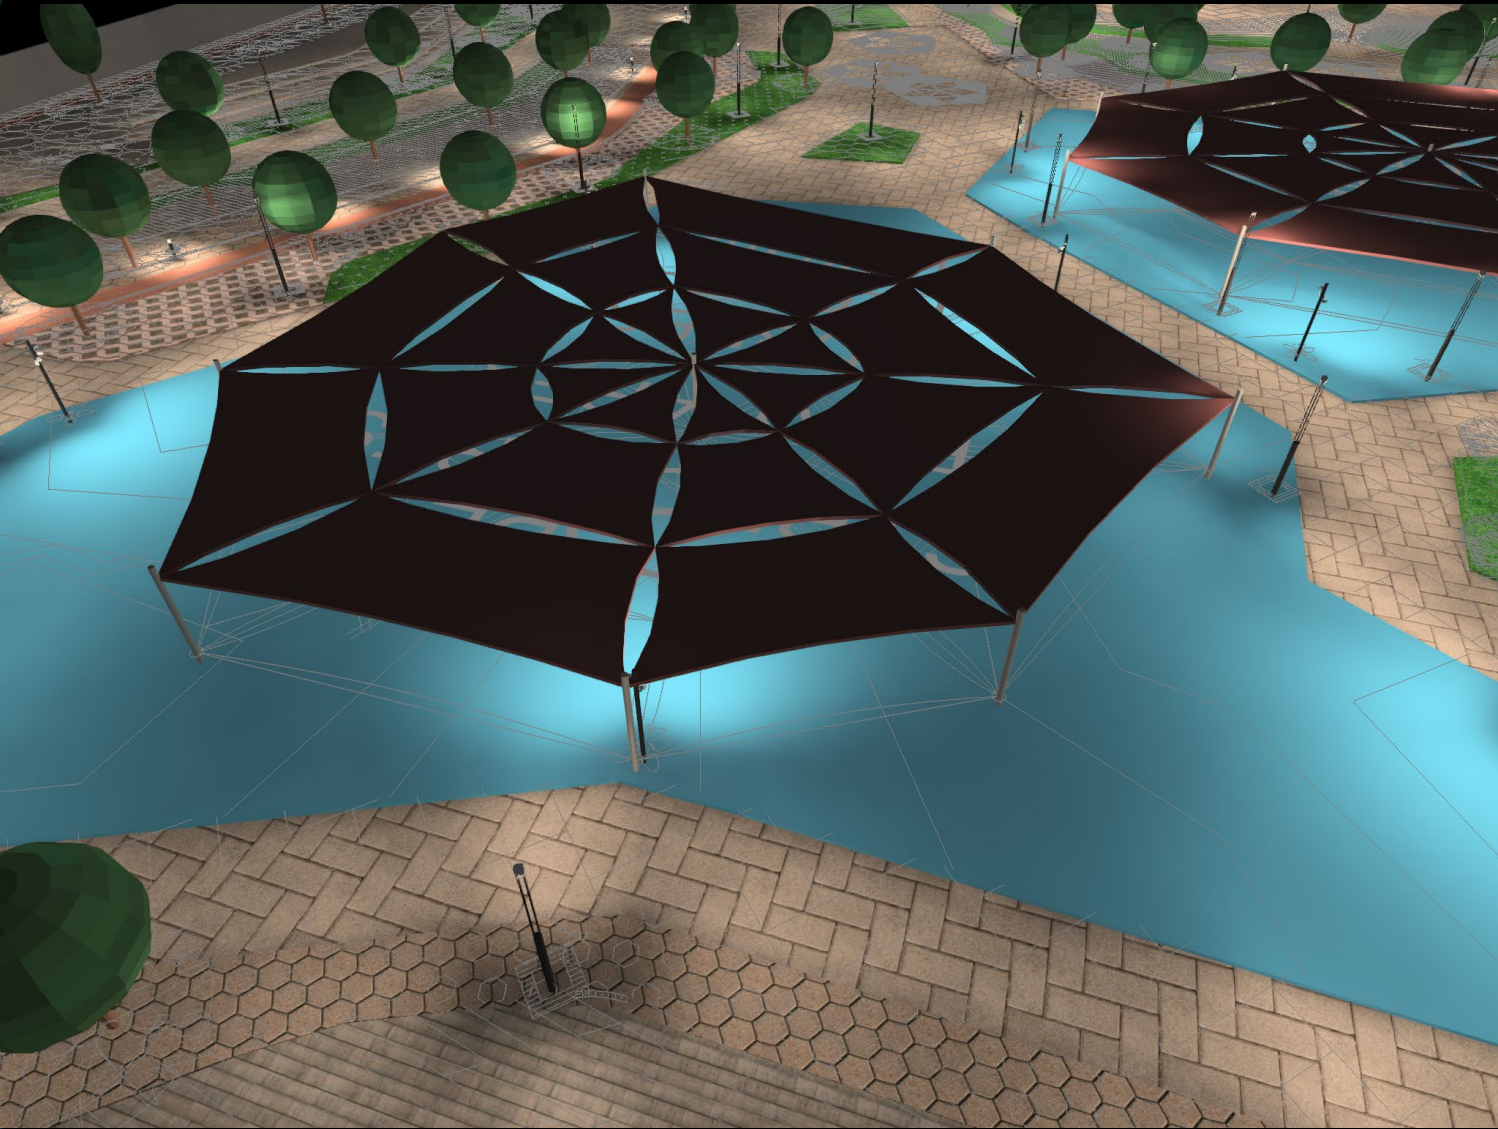


Properties


Ē

11- Shade Play Area 02
Perpendicular illuminance (adaptive)
Height: 0.200 m


29.0 lx

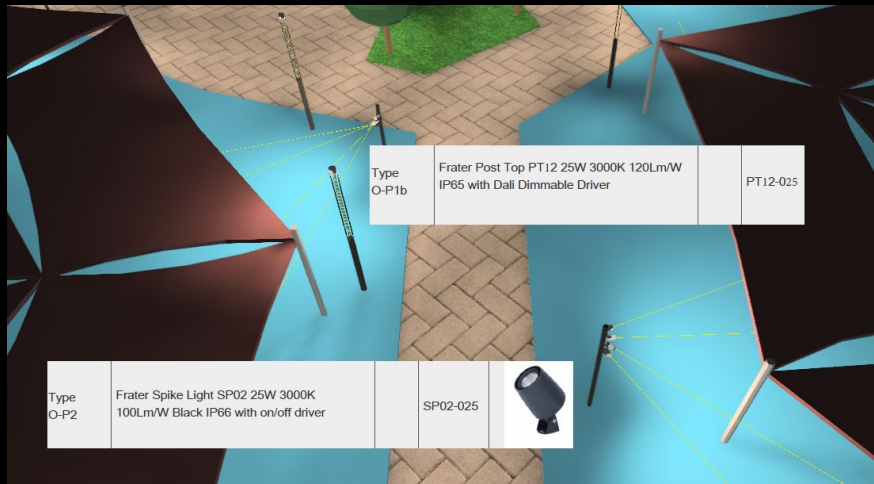


Notes :

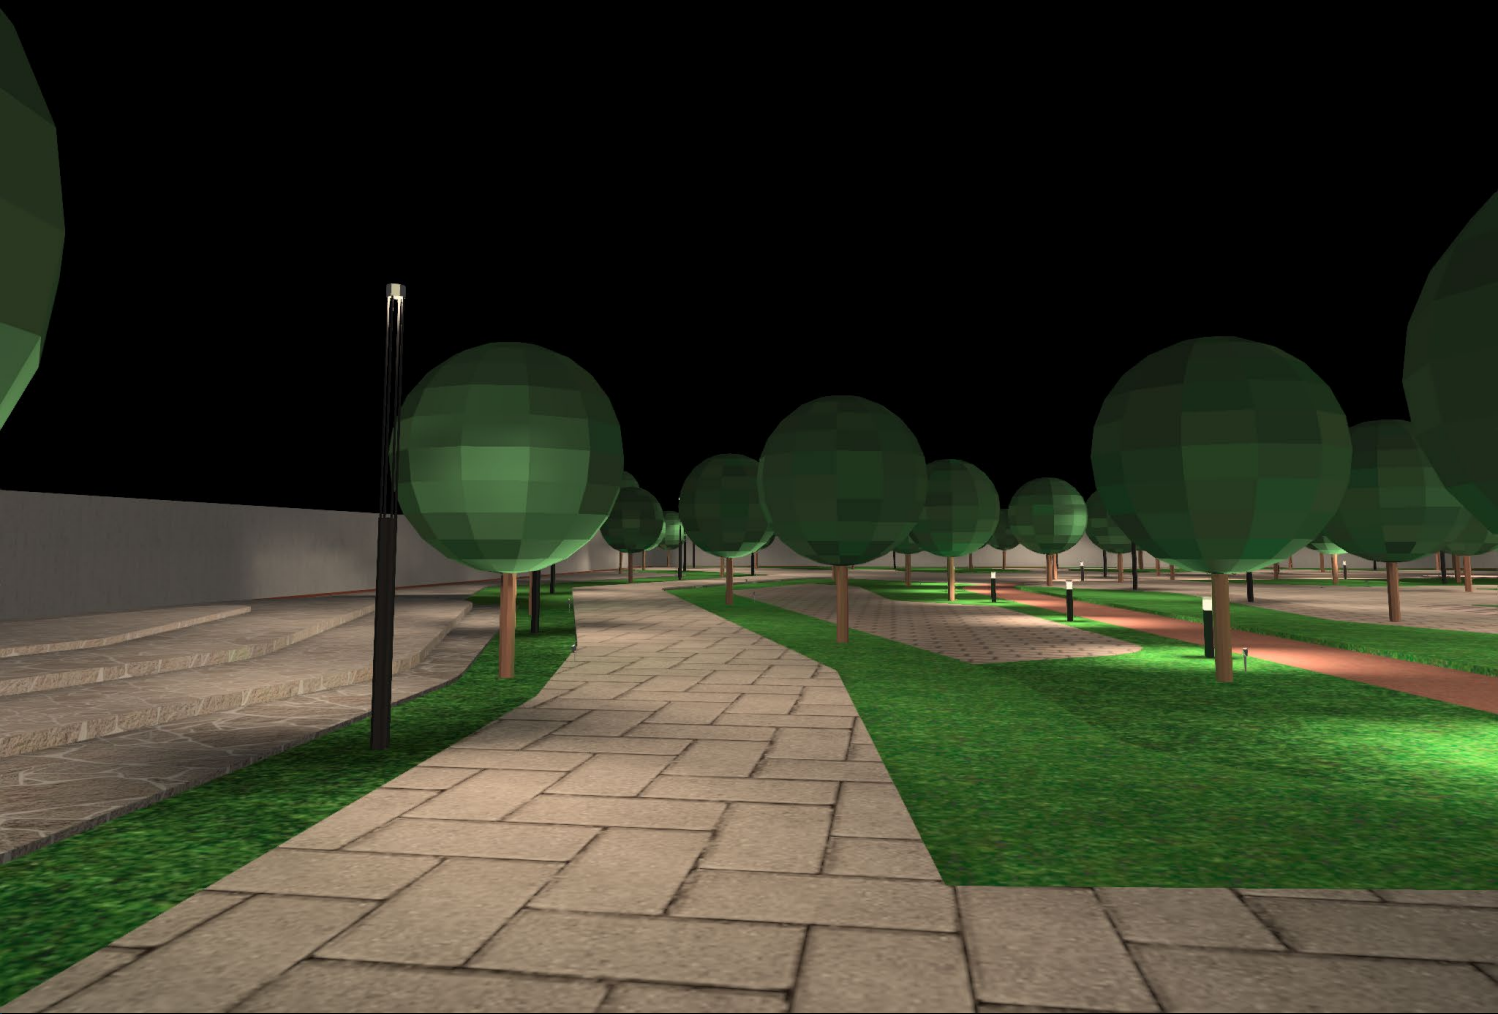

Properties	$\bar{E}$
12- Pathway 01 Perpendicular illuminance (adaptive) Height: 0.200 m	14.8 lx

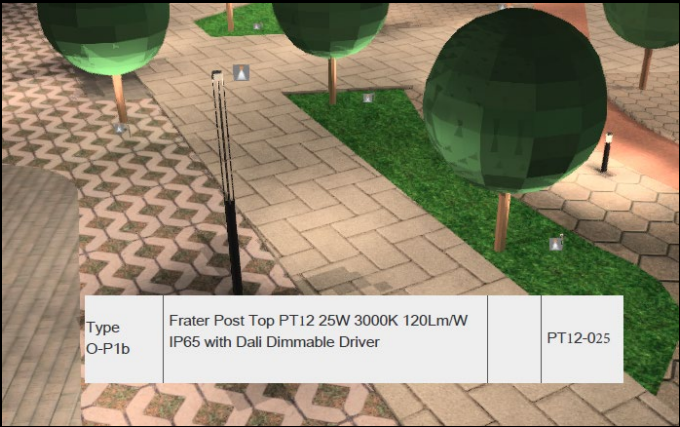

Notes :

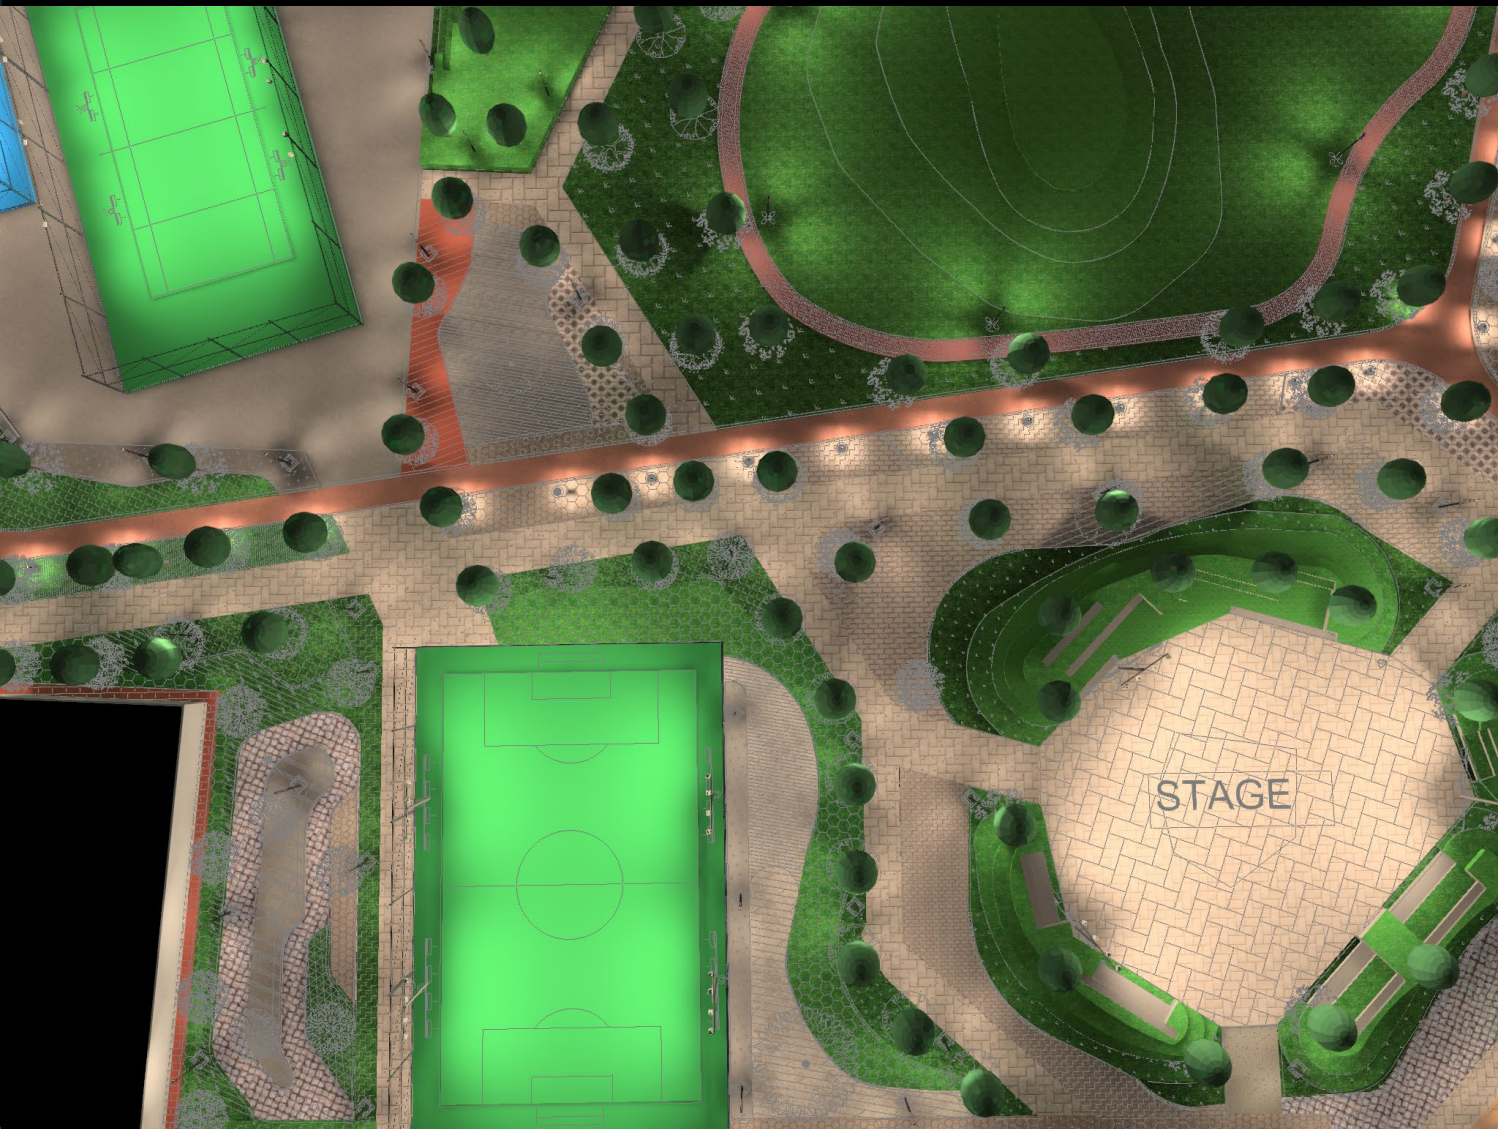


Properties

$\bar{E}$

13- Pathway 02
Perpendicular illuminance (adaptive)
Height: 0.100 m


16.3 lx

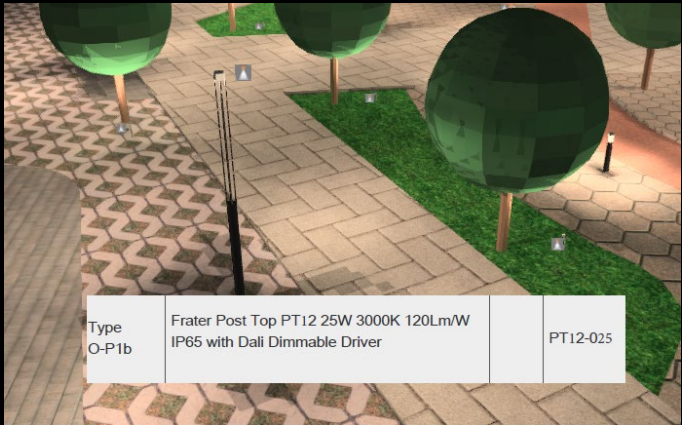

Type O-P1b	Frater Post Top PT12 25W 3000K 120Lm/W IP65 with Dali Dimmable Driver	PT12-025
---------------	--	----------

Notes :

Zone 14- Pathway 03

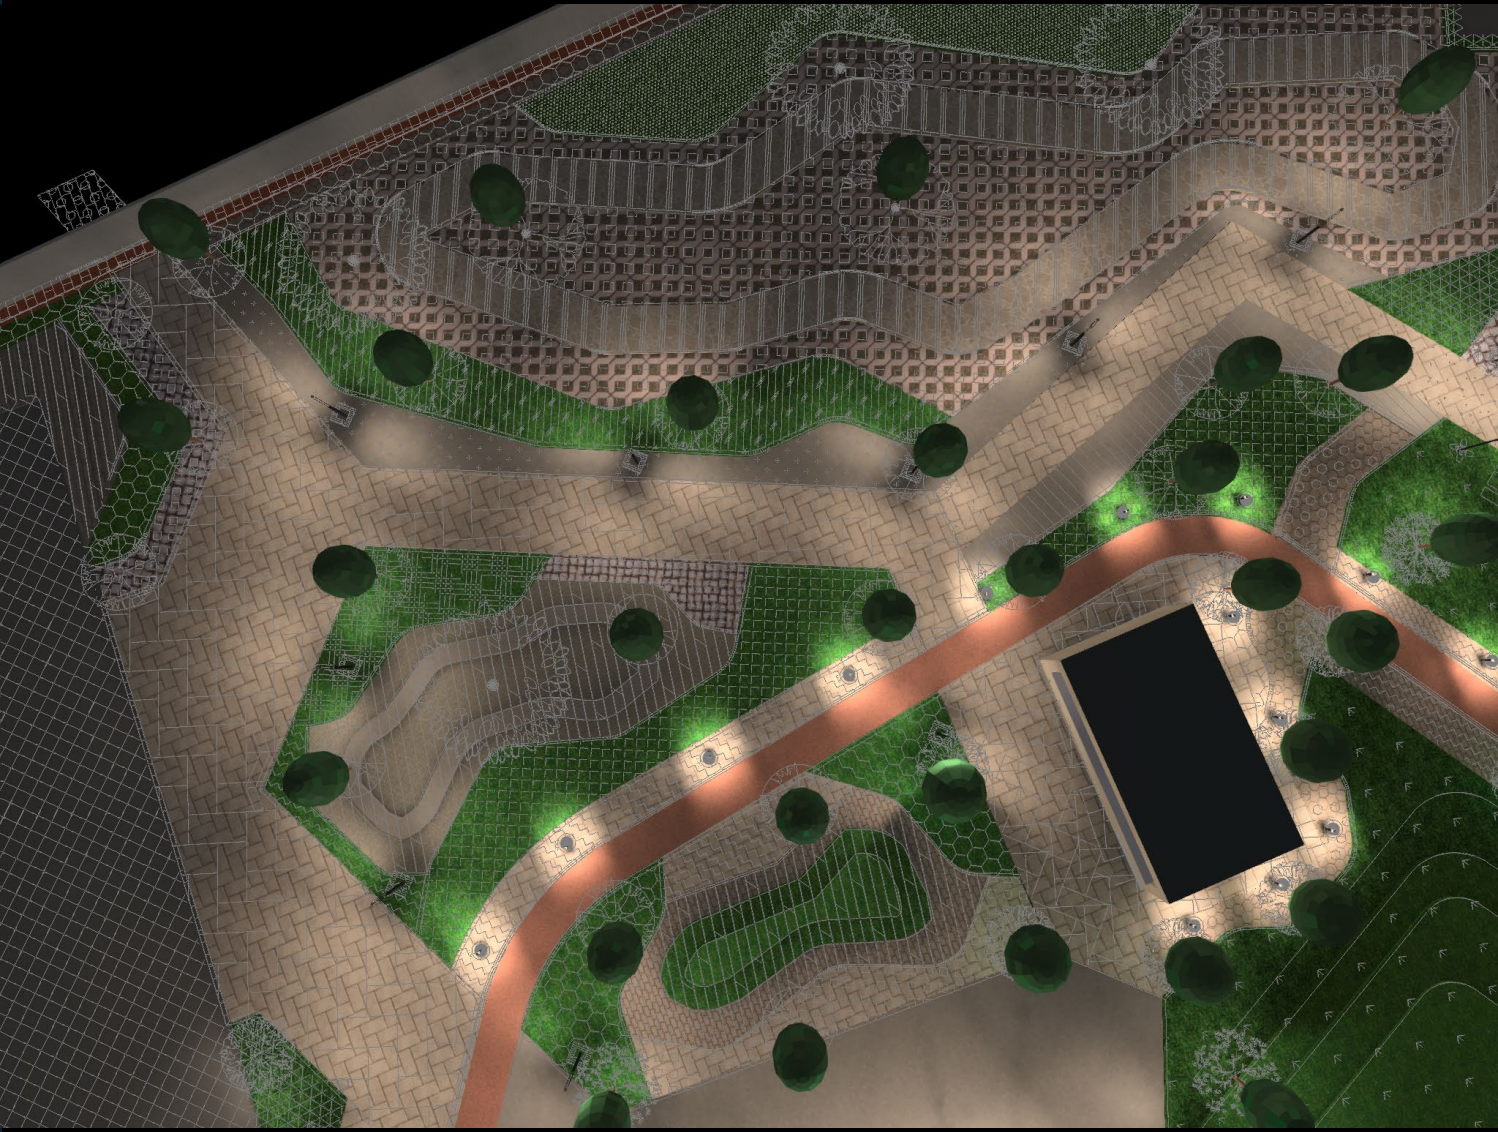

Properties	$\bar{E}$
14- Pathway 03	9.97 lx
Perpendicular illuminance (adaptive)	
Height: 0.100 m	



Type O-P1b	Frater Post Top PT12 25W 3000K 120Lm/W IP65 with Dali Dimmable Driver	PT12-025
---------------	--	----------

Notes :

Zone 15- Big Lawn




Properties	Ē
15- Big Lawn Zone 01 Perpendicular illuminance (adaptive) Height: 0.200 m	13.4 lx
15- Big Lawn Zone 02 Perpendicular illuminance (adaptive) Height: 0.300 m	8.17 lx
15- Big Lawn Zone 03 Perpendicular illuminance (adaptive) Height: 0.400 m	3.28 lx



Type O-P2	Frater Spike Light SP02 25W 3000K 100Lm/W Black IP66 with on/off driver	SP02-025	
--------------	--	----------	--

Notes :

Zone 16- Open Area

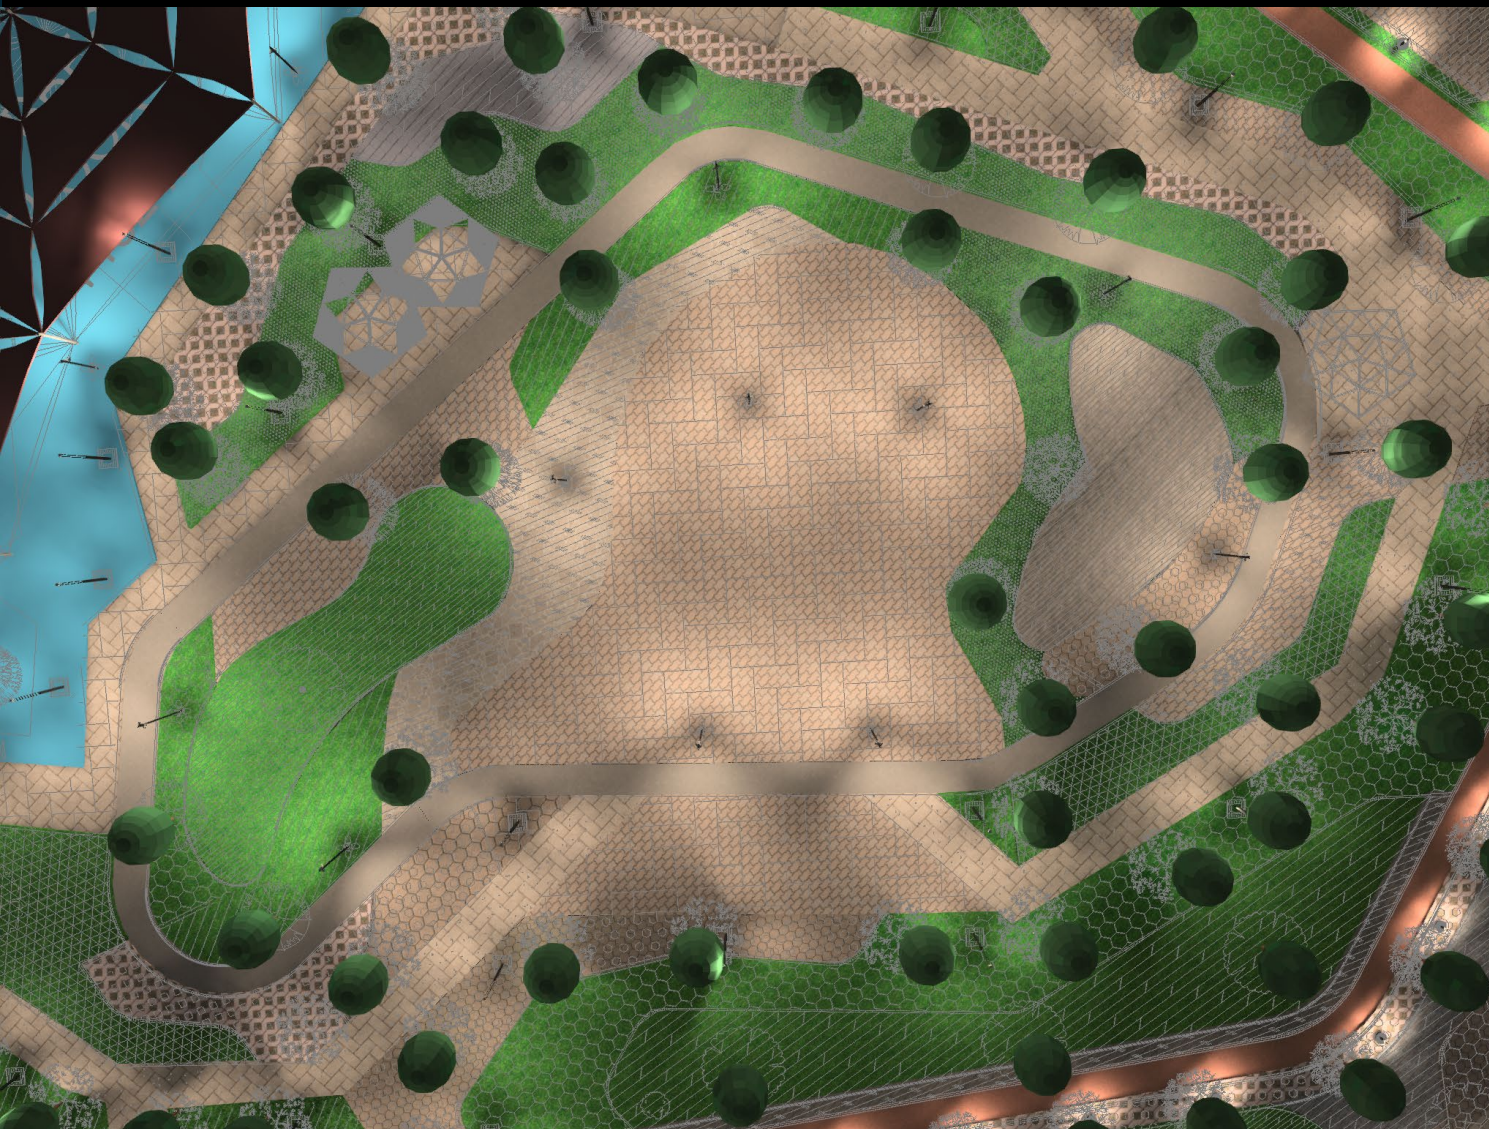

Properties

Ē

16- Open Area
Perpendicular illuminance (adaptive)
Height: 0.200 m

36.8 lx



Type O-P2	Frater Spike Light SP02 25W 3000K 100Lm/W Black IP66 with on/off driver	SP02-025	
--------------	--	----------	--

Notes :